


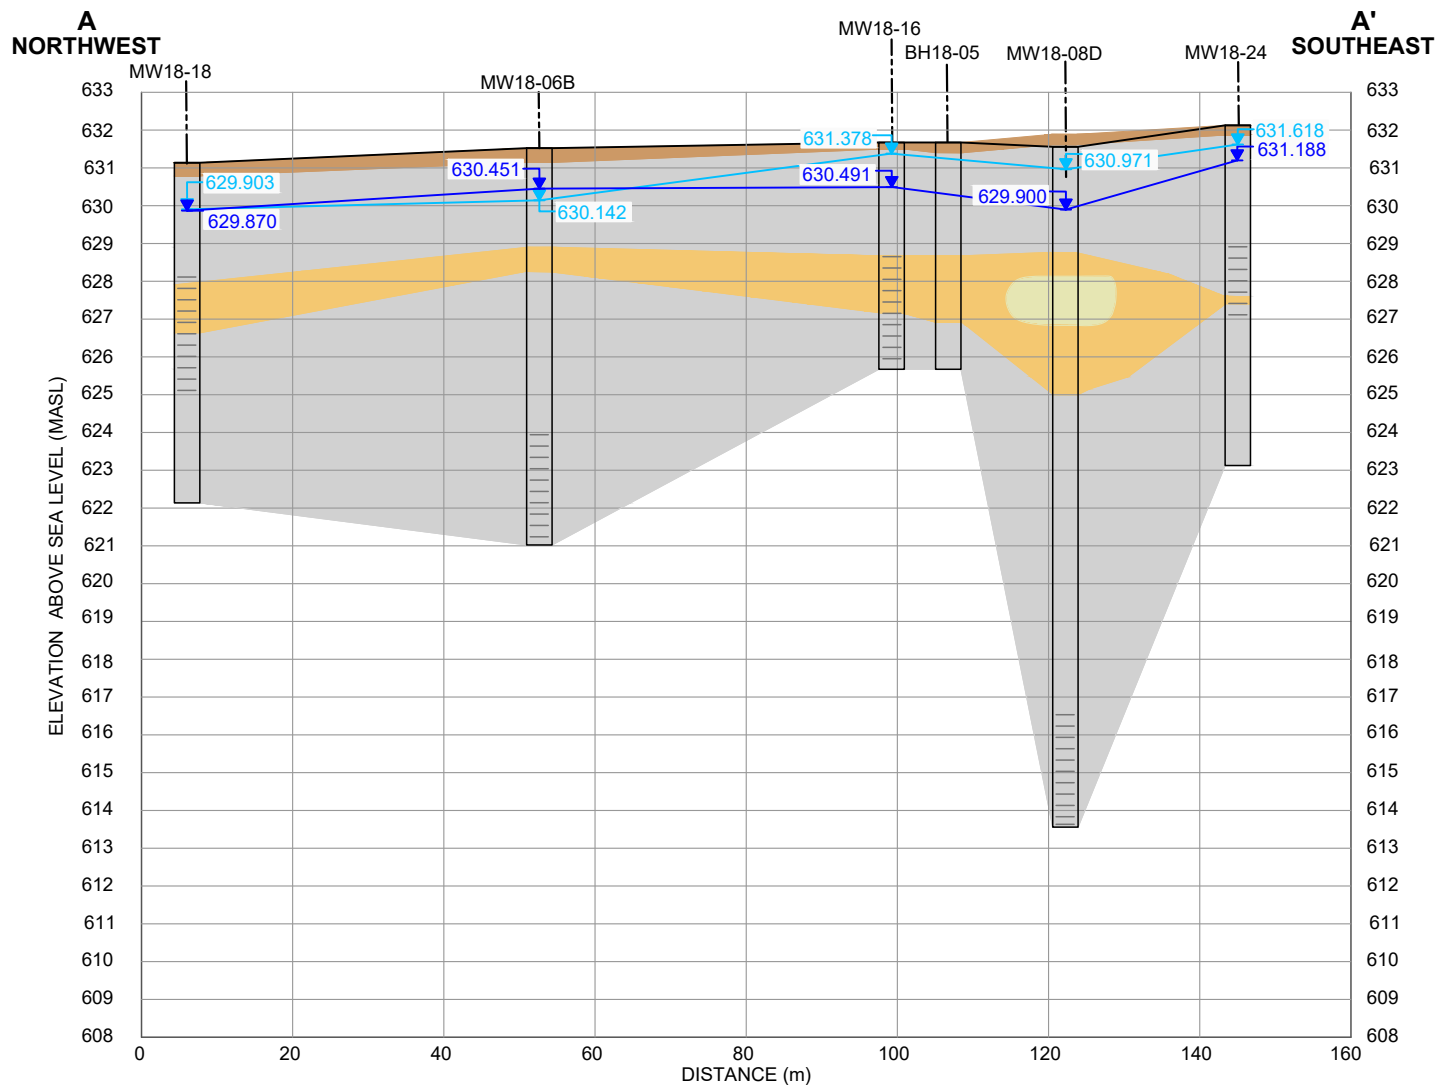

0 10 20 30
1:1 000 Metres

NOTE: masl DENOTES METRES ABOVE SEA LEVEL

LEGEND

- TOPSOIL
- SAND
- SAND AND CLAY
- CLAY
- SCREENED INTERVAL
- GROUNDWATER LEVEL (MAY 2024)
- GROUNDWATER LEVEL (JUNE 2025)
- GROUNDWATER ELEVATION masl (MAY 2024)
- GROUNDWATER ELEVATION masl (JUNE 2025)

PROJECT 100/09-29 & 100/16-29-057-19 W4M

TITLE
CROSS SECTION A - A'
WITH GROUNDWATER LEVELS

SOURCE ECOVENTURE 2025

SCALE
1:1 000

DATE (MM/DD/YY)
05/11/26

DRAWN BY EC04/12/22-xsec
REVISED SL/JG

FIGURE NO.
3

PREPARED FOR:



PREPARED BY:

