



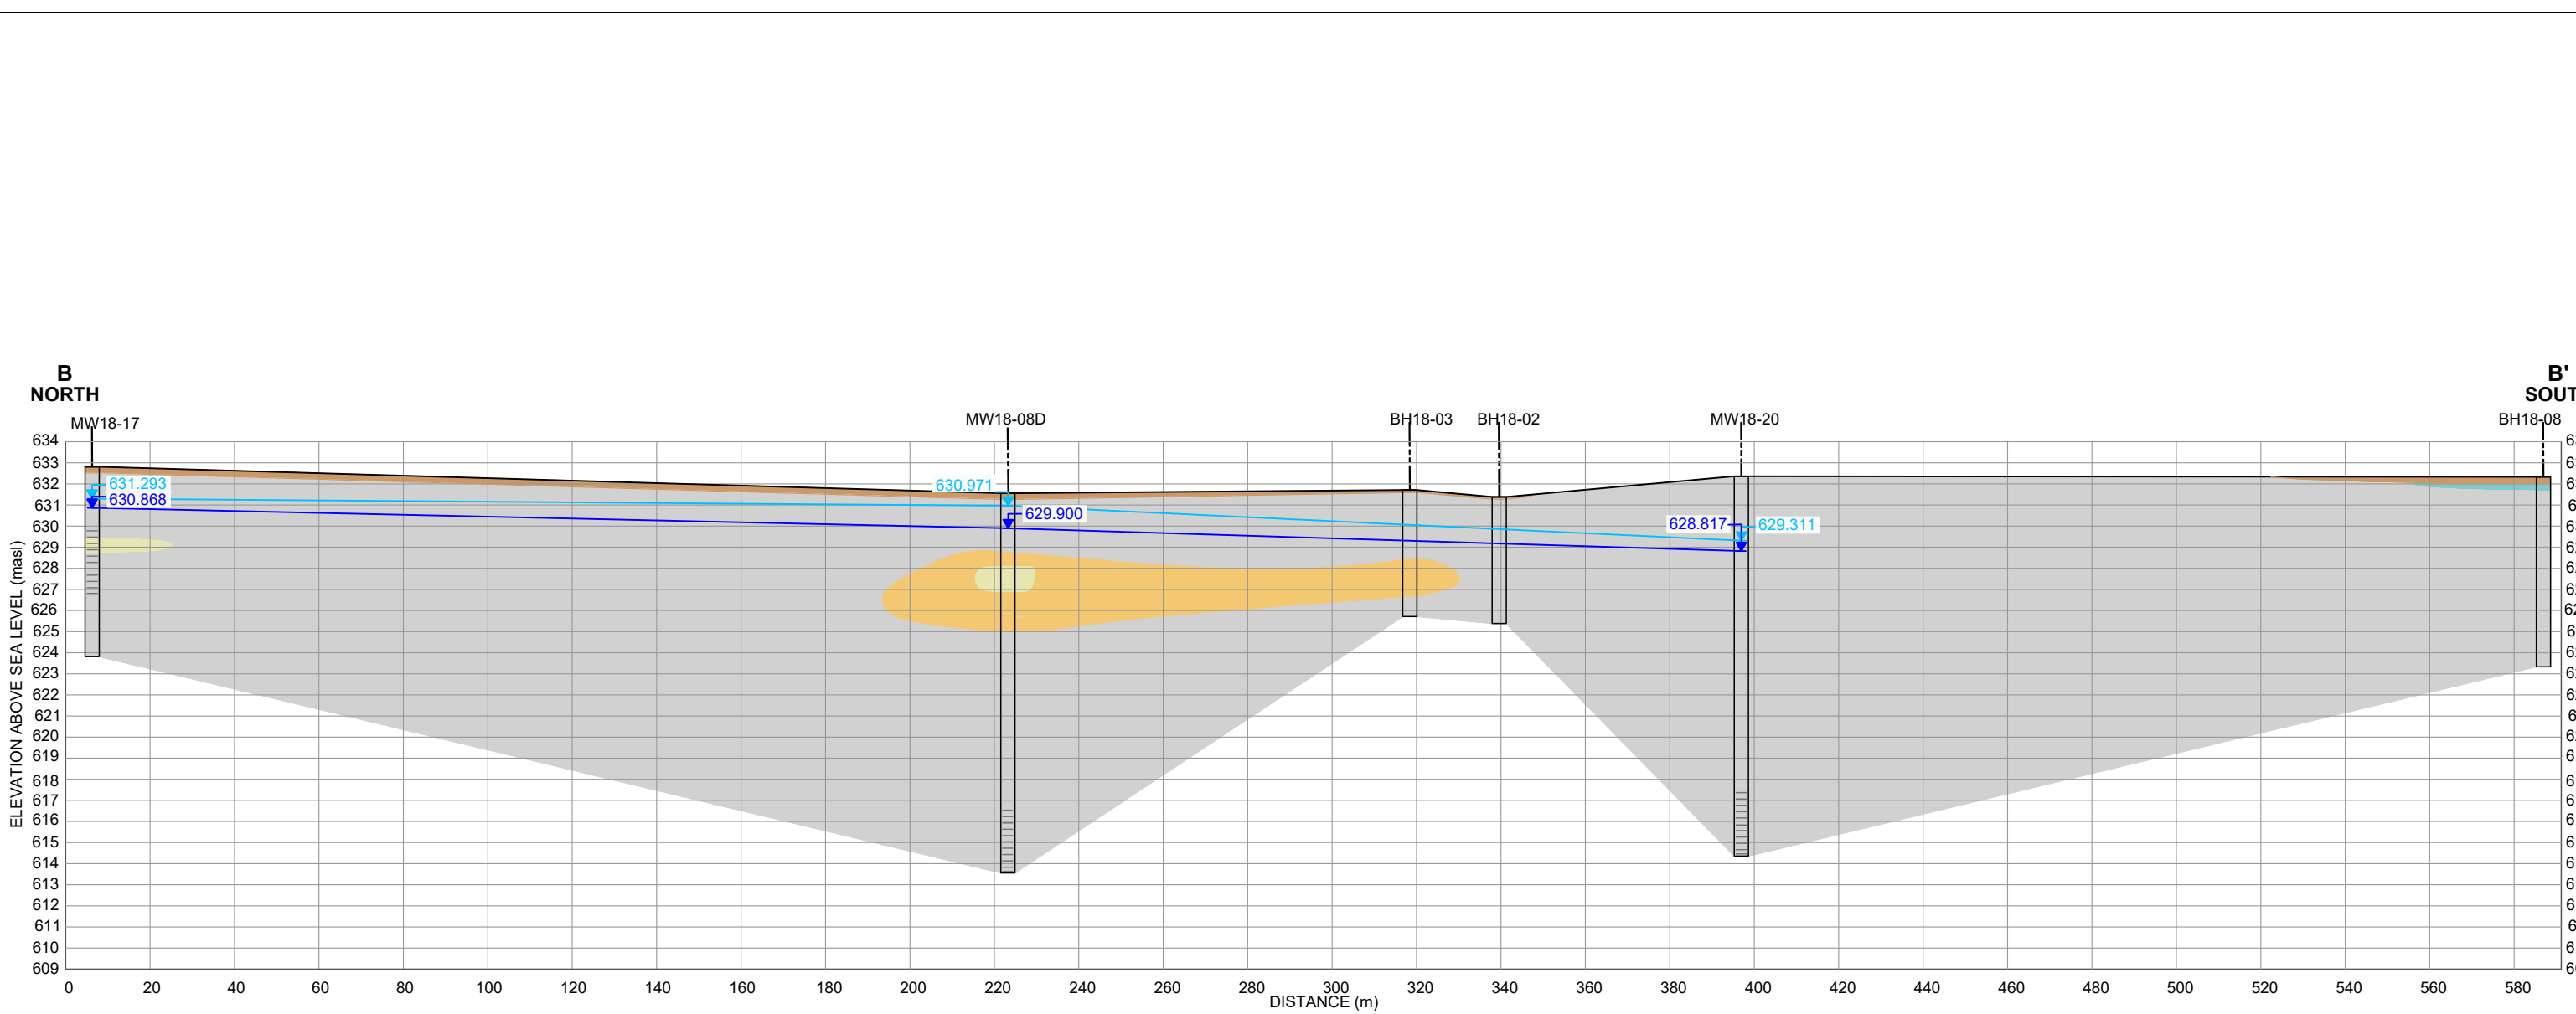

CROSS SECTION B - B'

SCALE 1:1 500
5x VERTICAL EXAGGERATION

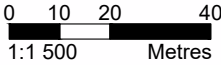

LEGEND	
	TOPSOIL
	SAND
	SAND AND CLAY
	SILT
	CLAY
	SCREENED INTERVAL
	GROUNDWATER LEVEL (MAY 2024)
	GROUNDWATER LEVEL (JUNE 2025)
	GROUNDWATER ELEVATION masl (MAY 2024)
	GROUNDWATER ELEVATION masl (JUNE 2025)

PROJECT		100/09-29 & 100/16-29-057-19 W4M		PREPARED FOR:  PREPARED BY: 	NOTE: masl DENOTES METRES ABOVE SEA LEVEL
TITLE CROSS SECTION B - B'					
SOURCE ECOVENTURE 2025					
SCALE 1:1 500	DATE (MM/DD/YY) 05/11/26	DRAWN BY EC04/12/22-xsec REVISED SL/JG	FIGURE NO. 4		