



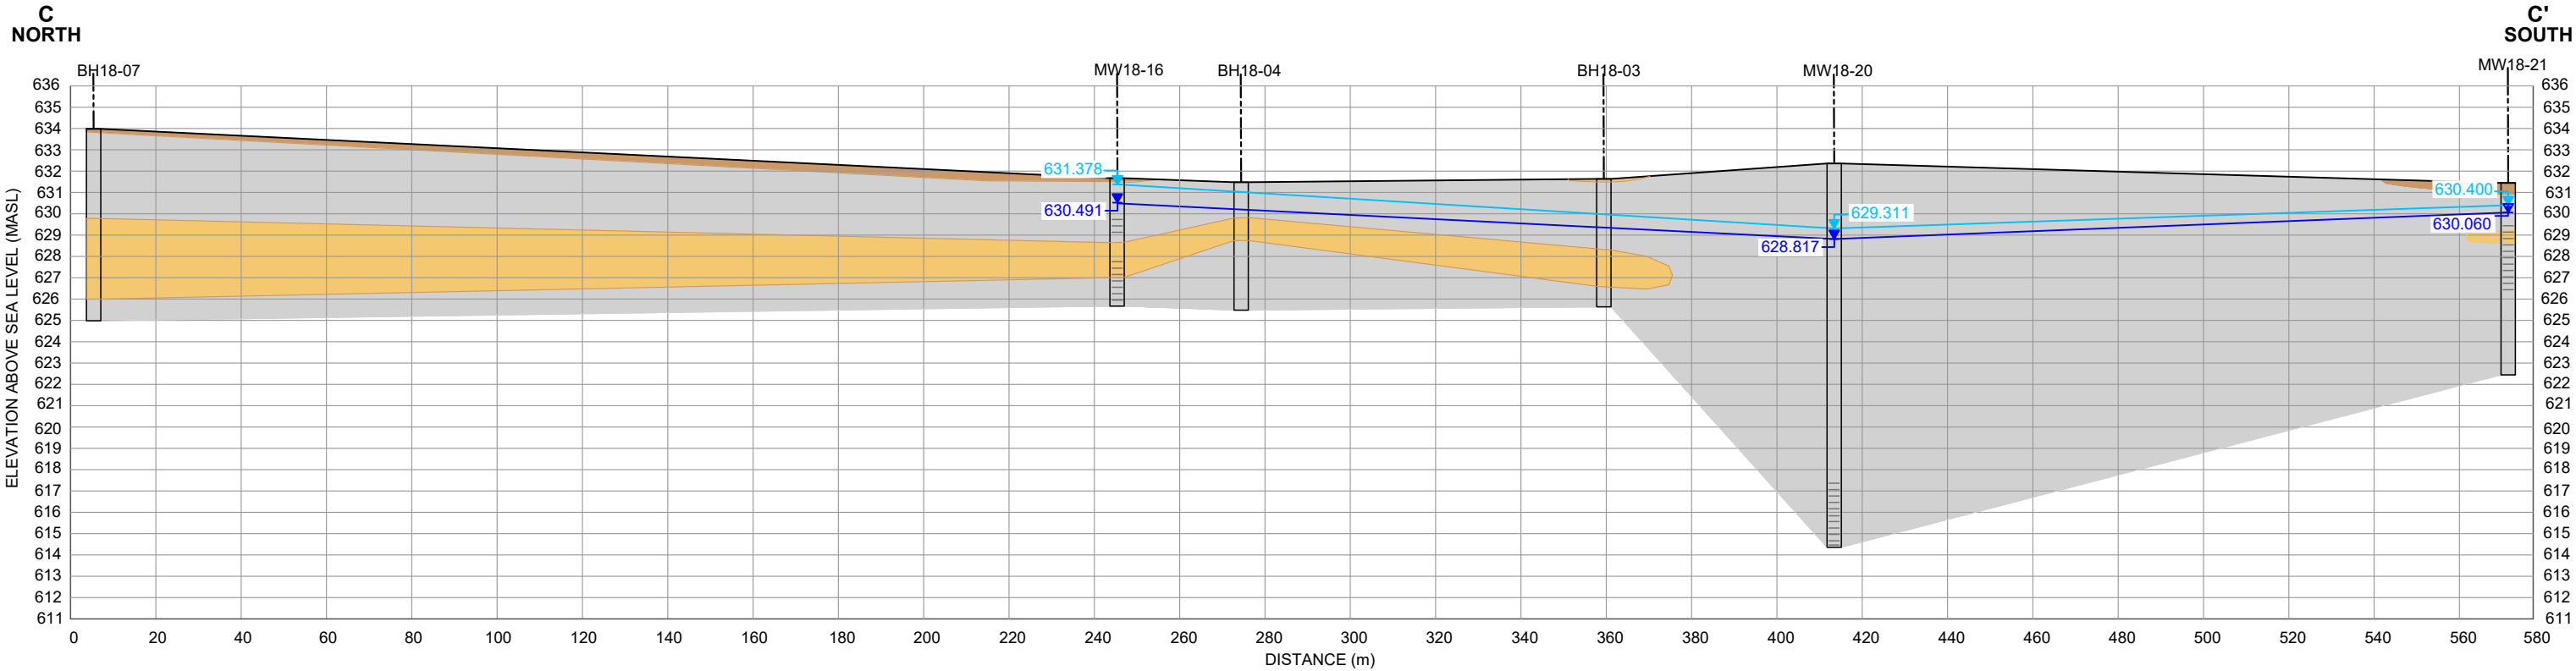

CROSS SECTION C - C'
SCALE 1:1 500
5x VERTICAL EXAGGERATION

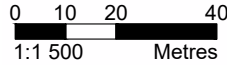

LEGEND	
	TOPSOIL
	SAND
	SAND AND CLAY
	CLAY
	GROUNDWATER LEVEL (MAY 2024)
	GROUNDWATER LEVEL (JUNE 2025)
	GROUNDWATER ELEVATION masl (MAY 2024)
	GROUNDWATER ELEVATION masl (JUNE 2025)
	SCREENED INTERVAL

PROJECT 100/09-29 & 100/16-29-057-19 W4M			
TITLE CROSS SECTION C - C'			
SOURCE ECOVENTURE 2025			
SCALE 1:1 500	DATE (MM/DD/YY) 05/11/26	DRAWN BY EC04/12/22-xsec REVISED SL/JG	FIGURE NO. 5

PREPARED FOR:



PREPARED BY:



NOTE:
masl DENOTES METRES ABOVE SEA LEVEL